


Kopskats un galvenie izmēri

Uz kājām balstīts māla plaukts · Savienojumi un detaļas: S02-S07

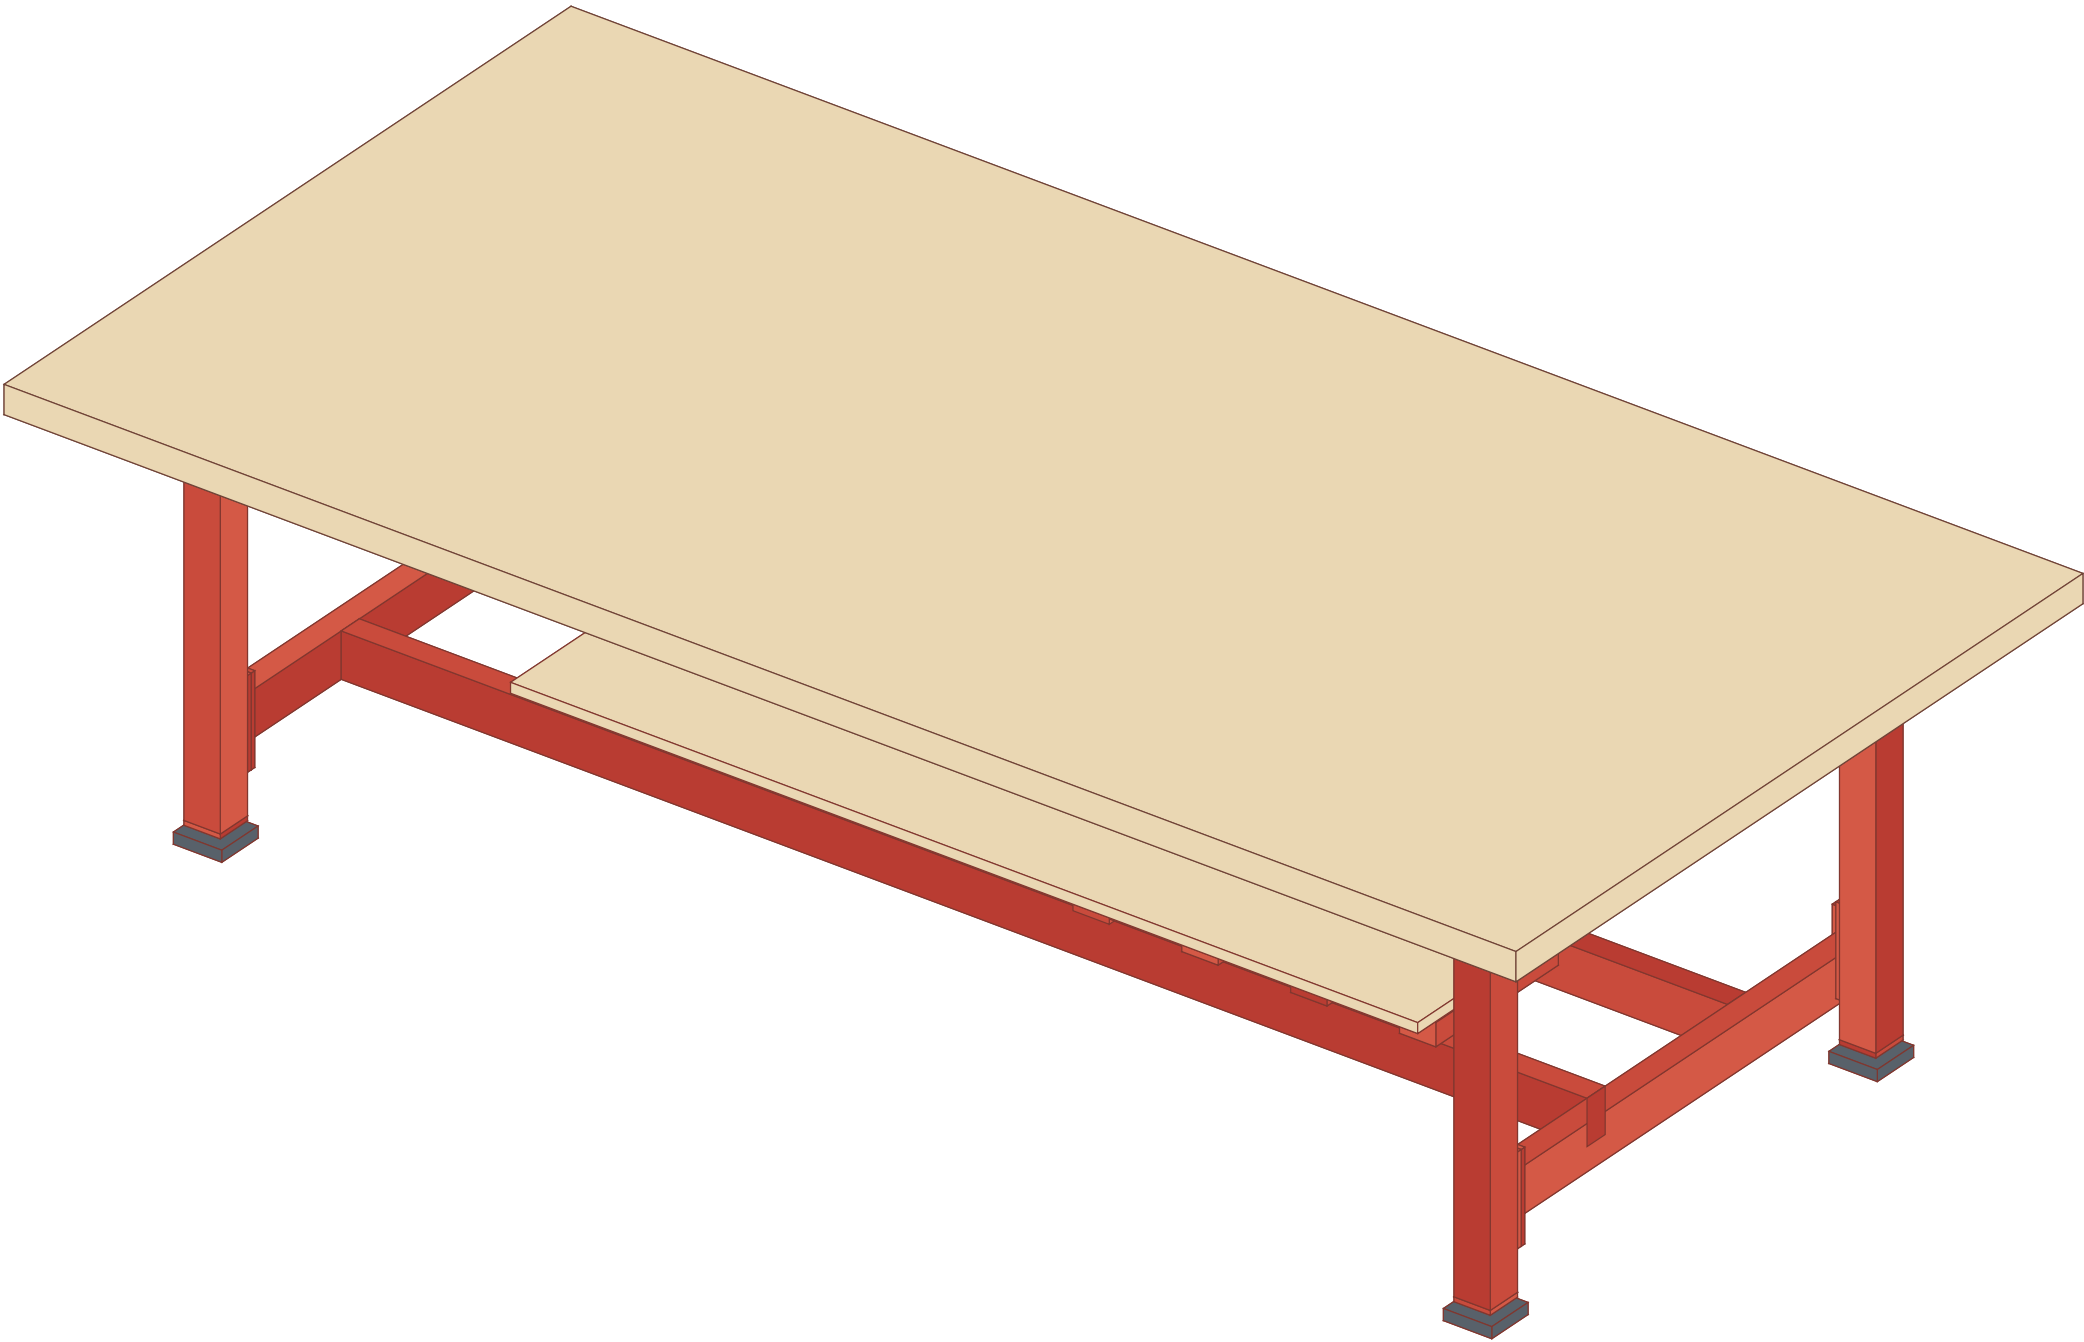

KONSTRUKCIJA

Virsmā: 250 × 125 × 5
Galda augstums: 78
Bērza saplāksnis; BB uz augšu
Tērauds: satīna RAL 3020

8 vietas; reizēm 10
4 noņemamas kājas
Plaukts pie visām 4 kājām

Plaukta slodzes mērķis: 200 kg

PĀRVADĀŠANA

Virsmā: 250 × 125
Augšējais rāmis: 230 × 105
Plaukta mezgls: 216 × 77,4
Klājs atsevišķi: 150 × 35

Vispirms atskrūvēt plauktu.
Tad atskrūvēt kājas.


DARBA VIETA
Pa trim sēdvietām gar sāniem,
pa vienai katrā galā.

VIETA KĀJĀM
Klājs 45 no sāniem, 50 no galiem.
Gala šķērssijas Z=15-23.

SLODZE
Maisi → klājs → sijas → kājas.
200 kg ir projektēšanas mērķis.

Augšējais rāmis — plāns

Mērogs 1:10 uz A3 · X galda garumā, Y platumā · Virsma noņemta

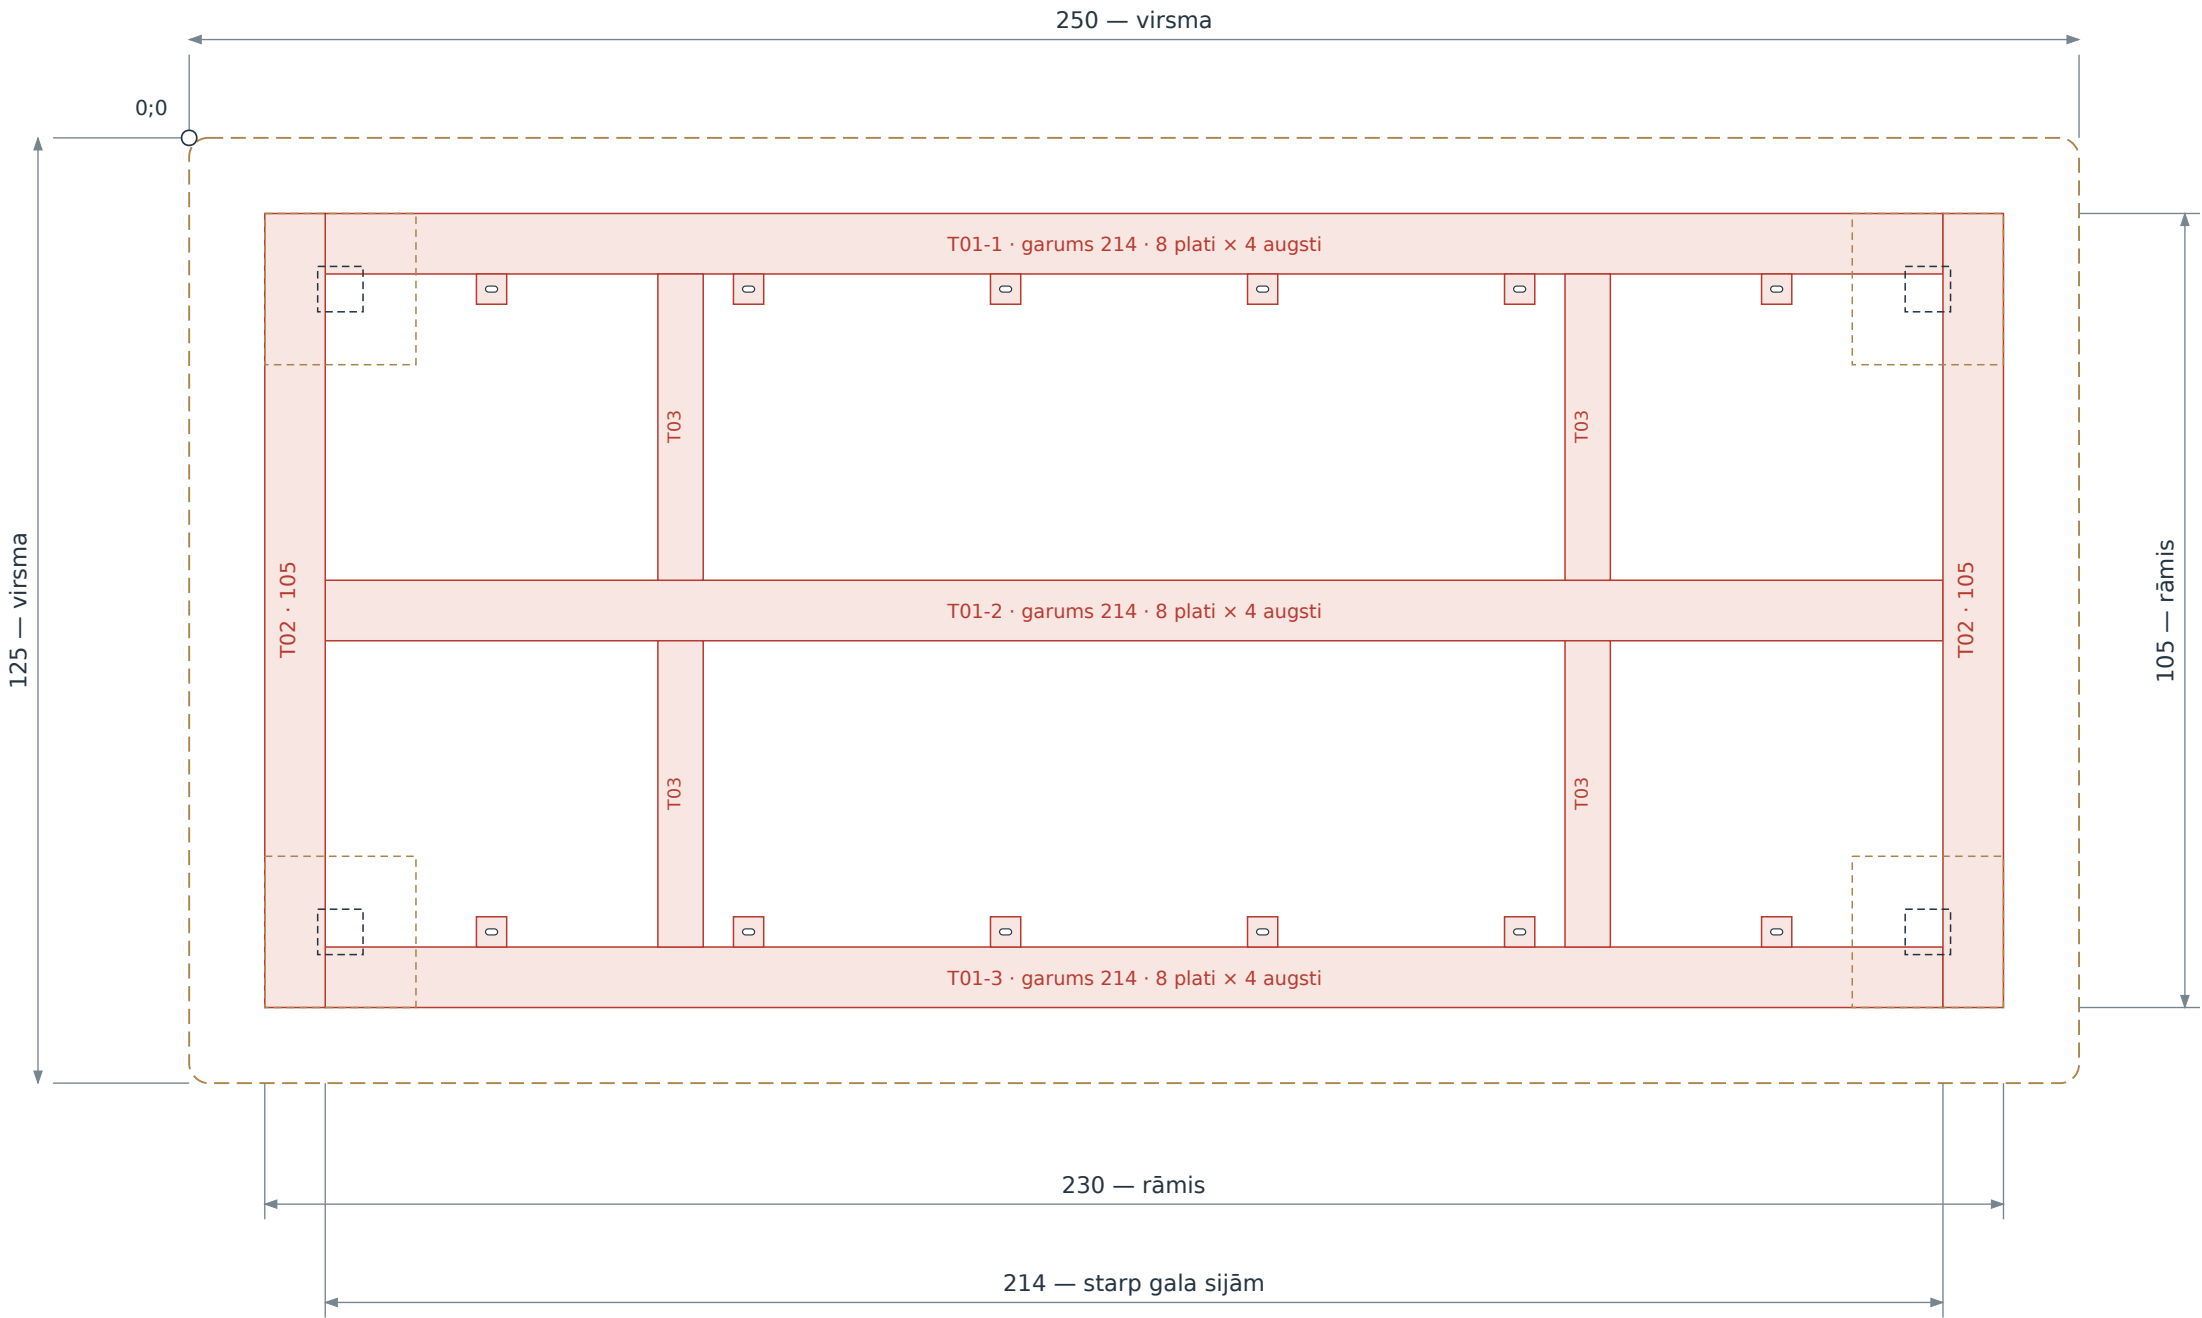

KOORDINĀTAS

Rāmis X: 10–240

Rāmis Y: 10–115

T02 X: 10–18

un 232–240

T01 Y: 10–18;

58,5–66,5; 107–115

T03 centri:

X=65 un 185

Augšējā plakne Z=72,8.

Abiem profiliem 4 vertikāli.

Diagonāle: 252,83 · Diagonāļu starpība ≤0,2 · Balsta plaknes novirze ≤0,15

P01 fiksētās plāksnes zem sijām parādītas pārtrauktā līnijā; kāju centri 20 no virsmas malām.


Uzgriežņu atveres izveidot pirms plākšņu piemetināšanas; urbt tikai caurules apakšējo sienu.

Rāmja sijas montēt ar taisniem galiem. Šuves, kas traucē virsmas balstīšanai, nolīdzināt.


Sānskatī un augstumu ķēde

Mērogs 1:10 uz A3 · Parādītas arī aizsegtās detaļas · Nomināli: virsma 5; klājs 1,8; EPDM 0,2

SKATS NO GARĀS MALAS

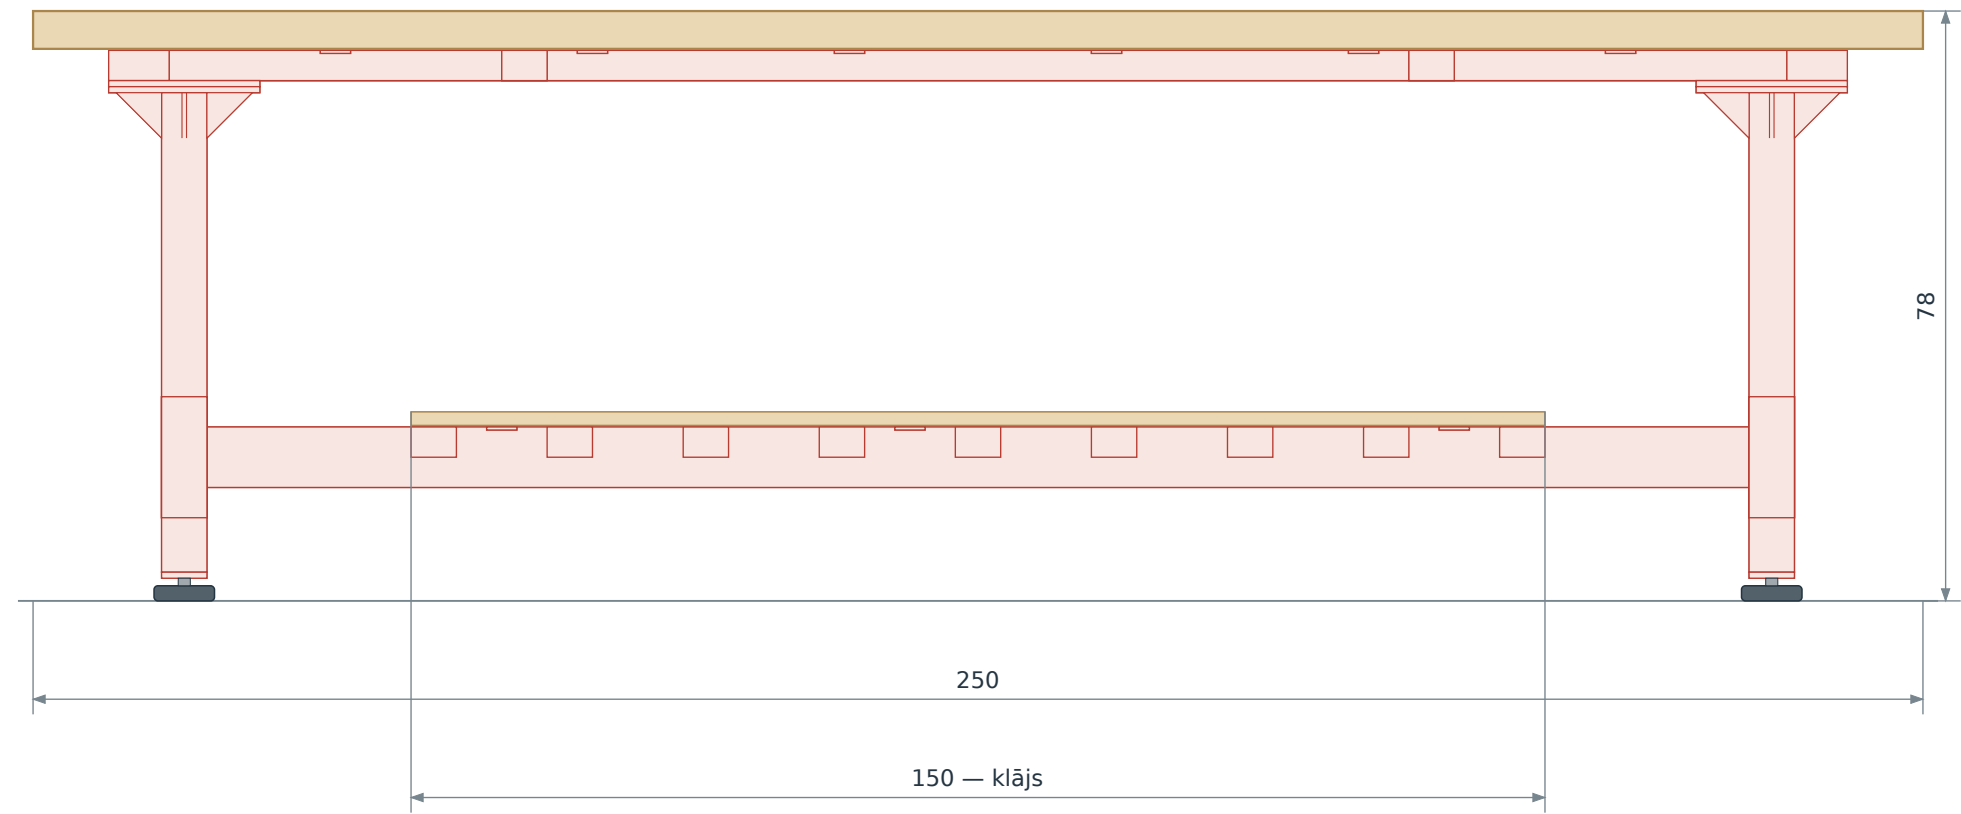

SKATS NO GALA

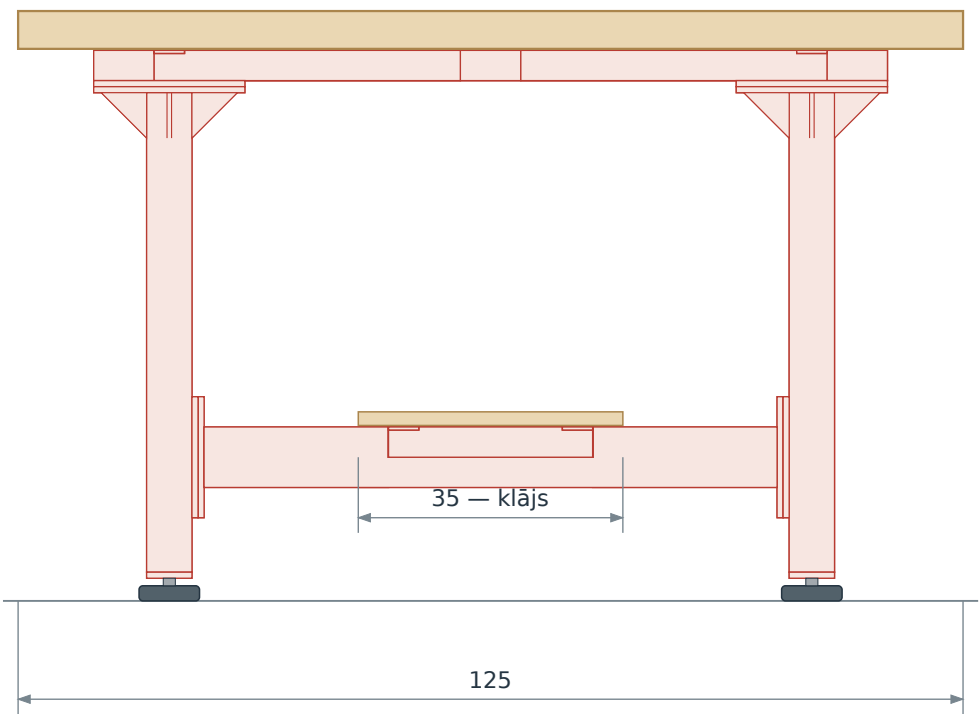

AUGSTUMI NO GRĪDAS


- 78 — gatavā galda virsma
- 73 — virsmas apakša
- 72,8 — tērauda balsta plakne
- 68,8 — augšējā rāmja apakša
- 68 — P01 plākšņu saskares plakne
- 67,2 — kājas caurules augša
- 3,8 — kājas caurules apakša
- 3 — P02 apakša; 0 — grīda

PLAUKTS UN REGULĒŠANA


- 25 — plaukta klāja augša; 23,2 — apakša.
- 23 — plaukta tērauda augša; 15 — siju apakša.
- Gala šķērssijas atrodas pie X=20 un 230.
- Pirms griešanas pārbaudīt krēslus un vietu pēdām.
- Balsta augstums = 8 – faktiskais virsmas biezums t.
- Pie t=4,81-5,15: balsts 3,19-2,85.
- Tērauda augstumi mainās par 5 – t; skatīt aprakstu.

Kāju augšējie mezgli un pēdas

P01 mērogā 1:1,5 · P02 mērogā 1:1 · Katras kājas augšā 4 skrūves M12

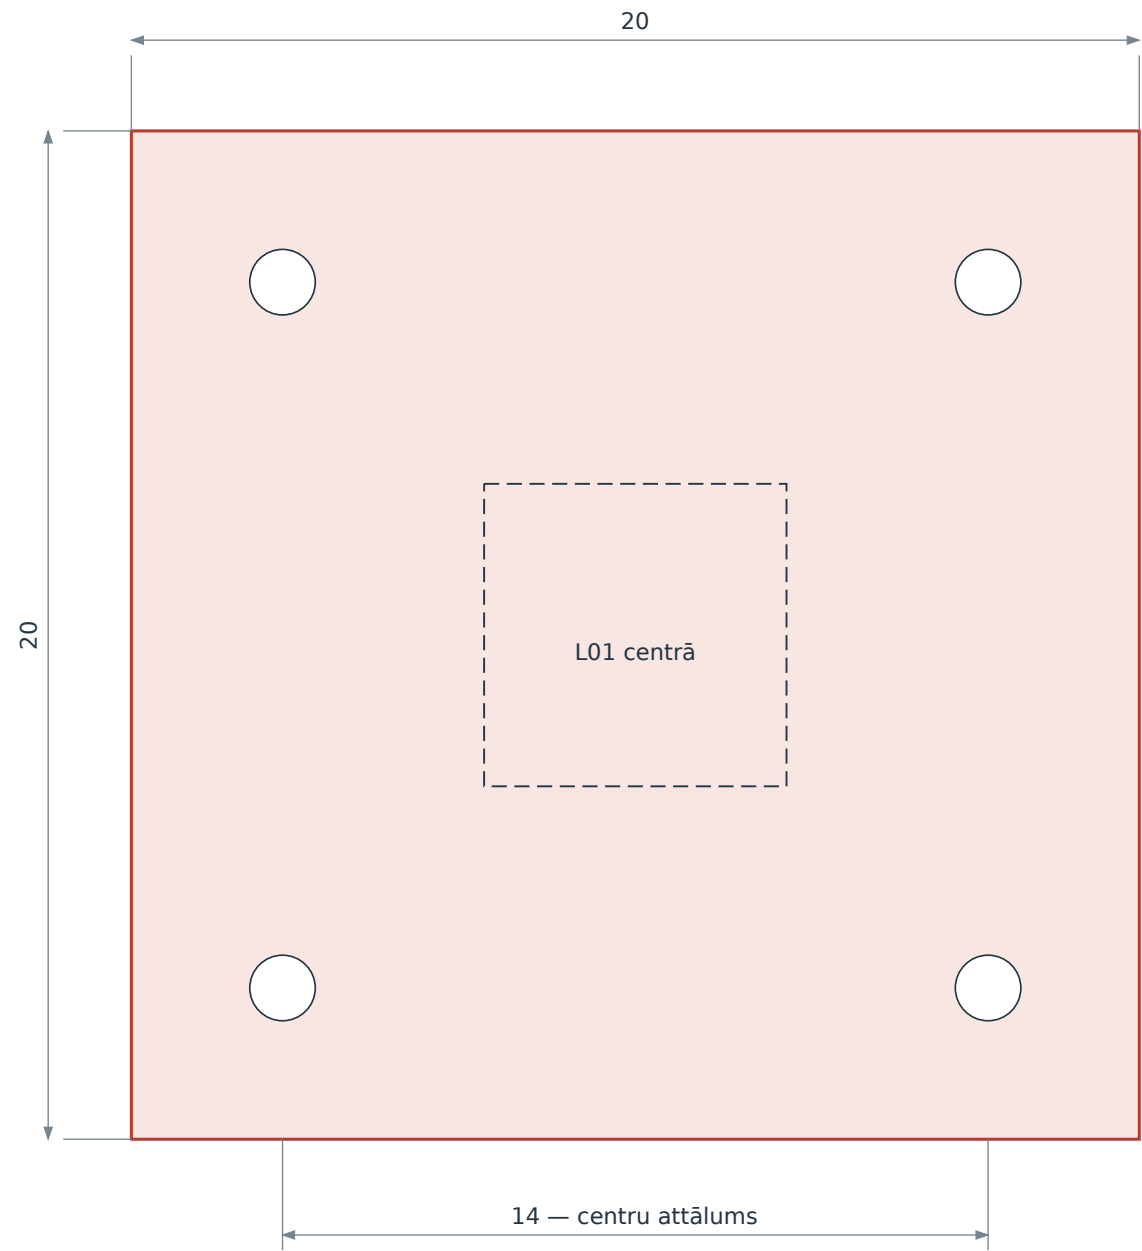


P01: 8 gab.; 20 × 20 × 0,8
4 urbumi Ø1,3; centri 3 no malām.
4 fiksētas un 4 noņemamas plāksnes.
Ribas kājas plakņu vidū; skrūves stūros.

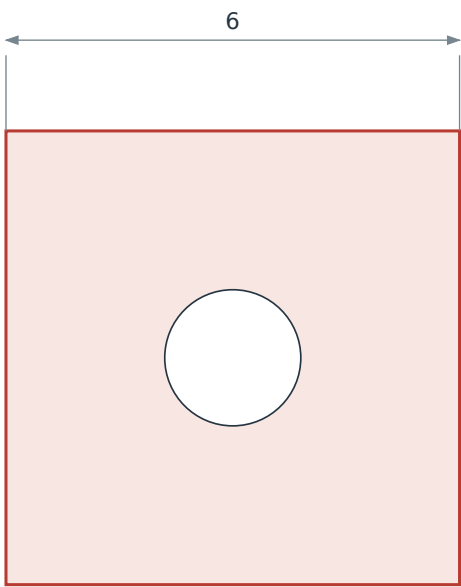

P02 · 6 × 6 × 0,8
Ø1,8 centrā, cauri plāksnei.
M16 uzgrieznis kājas iekšpusē.
Balstam pilna uzgriežņa saķere.
Kontruzgrieznis zem P02.

P05: 16 taisnleņķa ribas; katetes 6 un 6; biezums 0,6.
Ribas no Z=61,2 līdz 67,2; izvirzījums no caurules 6.
Kājas caurule: 6 × 6 × 0,3; garums 63,4.


AUGŠĒJĀ MEZGLA SHĒMA

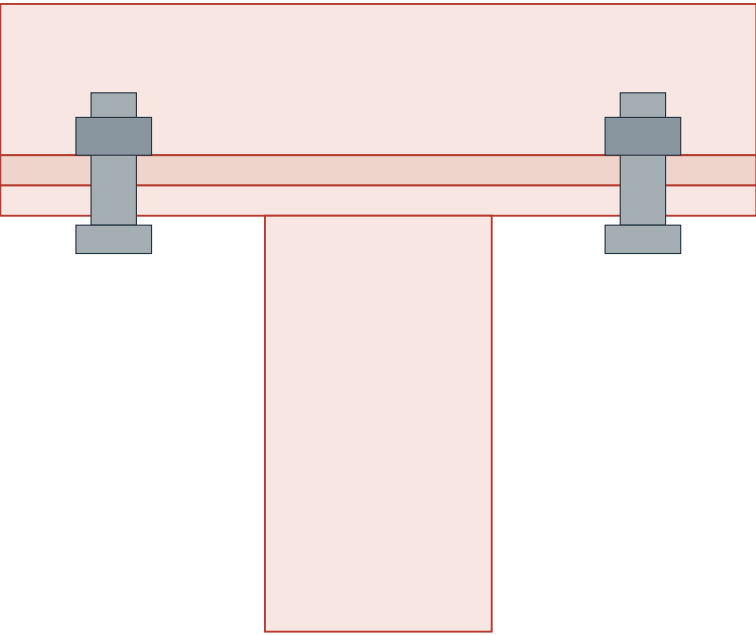

Rāmis 4 augsts; plāksnes 0,8 + 0,8.
M12 no apakšas; garums 3,5.
Ø3 atveres tikai caurules apakšā.
Pa 3 atverēm katrā stūrī.
Ceturtais uzgrieznis atklātā ailē.
Uzgriežņi virs fiksētās P01.

Plaukta rāmis un klājs

Plāns un sānskats mērogā 1:10 uz A3 · Metināts plaukta mezgls pieskrūvēts kājām

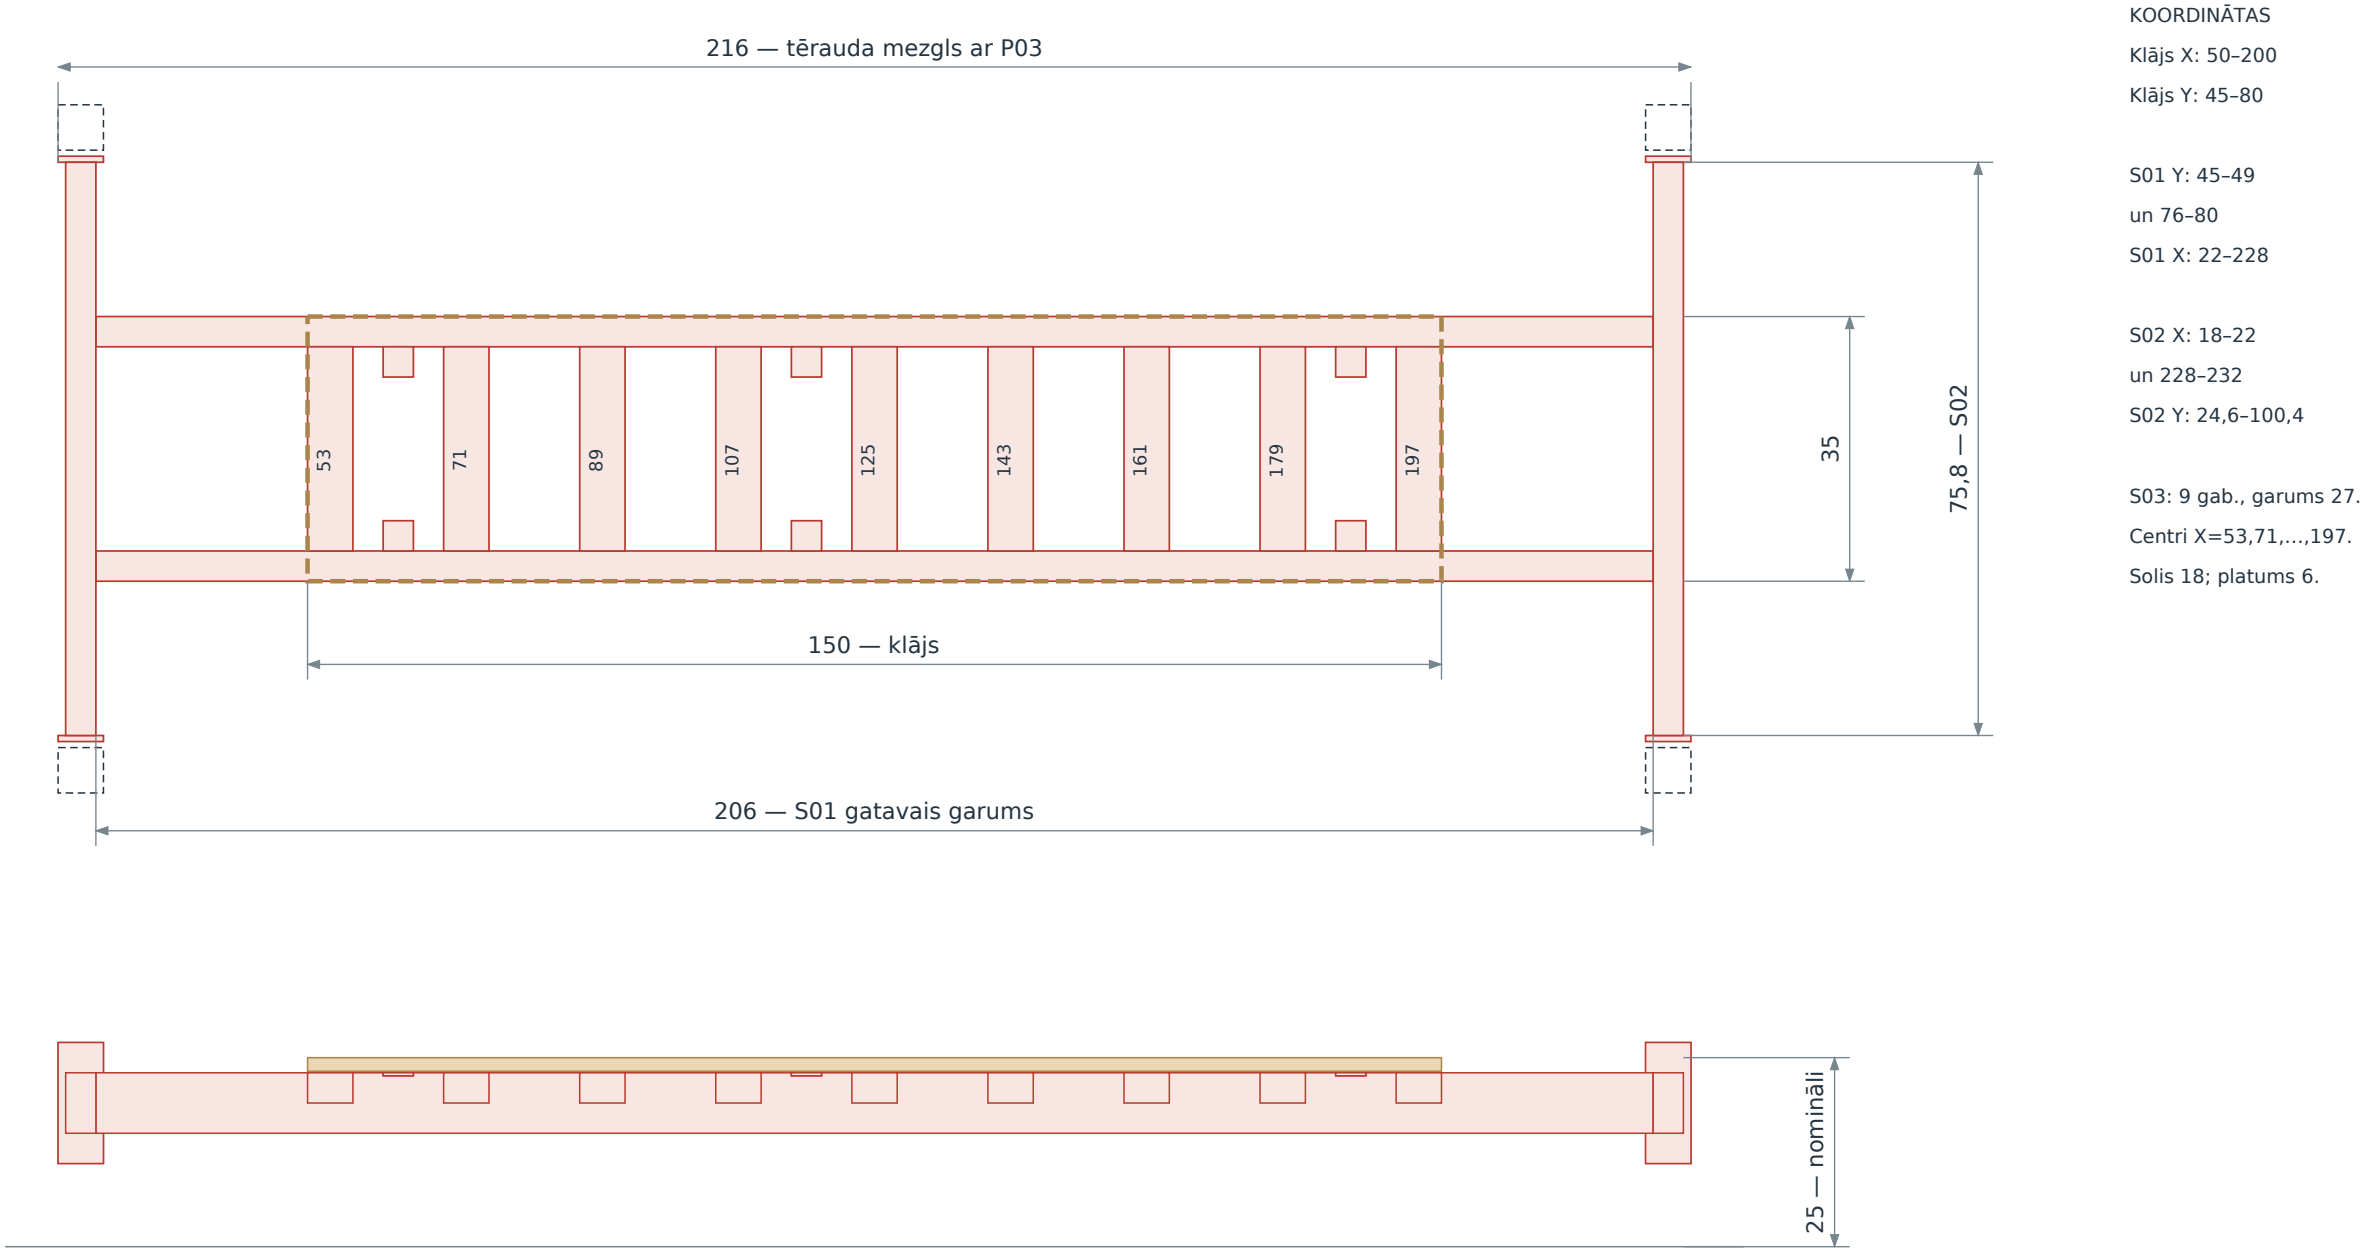

Sānskats ar aizsegtajām detaļām; EPDM 0,2 zem klāja.

S01 un S02: profils 8 × 4 × 0,3 ar 8 vertikāli. S03: profils 6 × 4 × 0,3 ar 4 vertikāli.


Siju augša Z=23; S01/S02 apakša Z=15; S03 apakša Z=19. Klāja augša nomināli Z=25.

Plaukta mezgla platums ar noņemamām P03: 77,4 (Y=23,8-101,2). Stiprinājumi: S07.

Līdz 200 kg vienmērīgi izvietotu maisu; neuzskatīt par sertificētu nestspēju.

Saplākšņa stiprinājumi


Plāns 1:10; skats caur virsmu no augšas, nevis spoguļots apakšskats · P04 mērogā 2:1

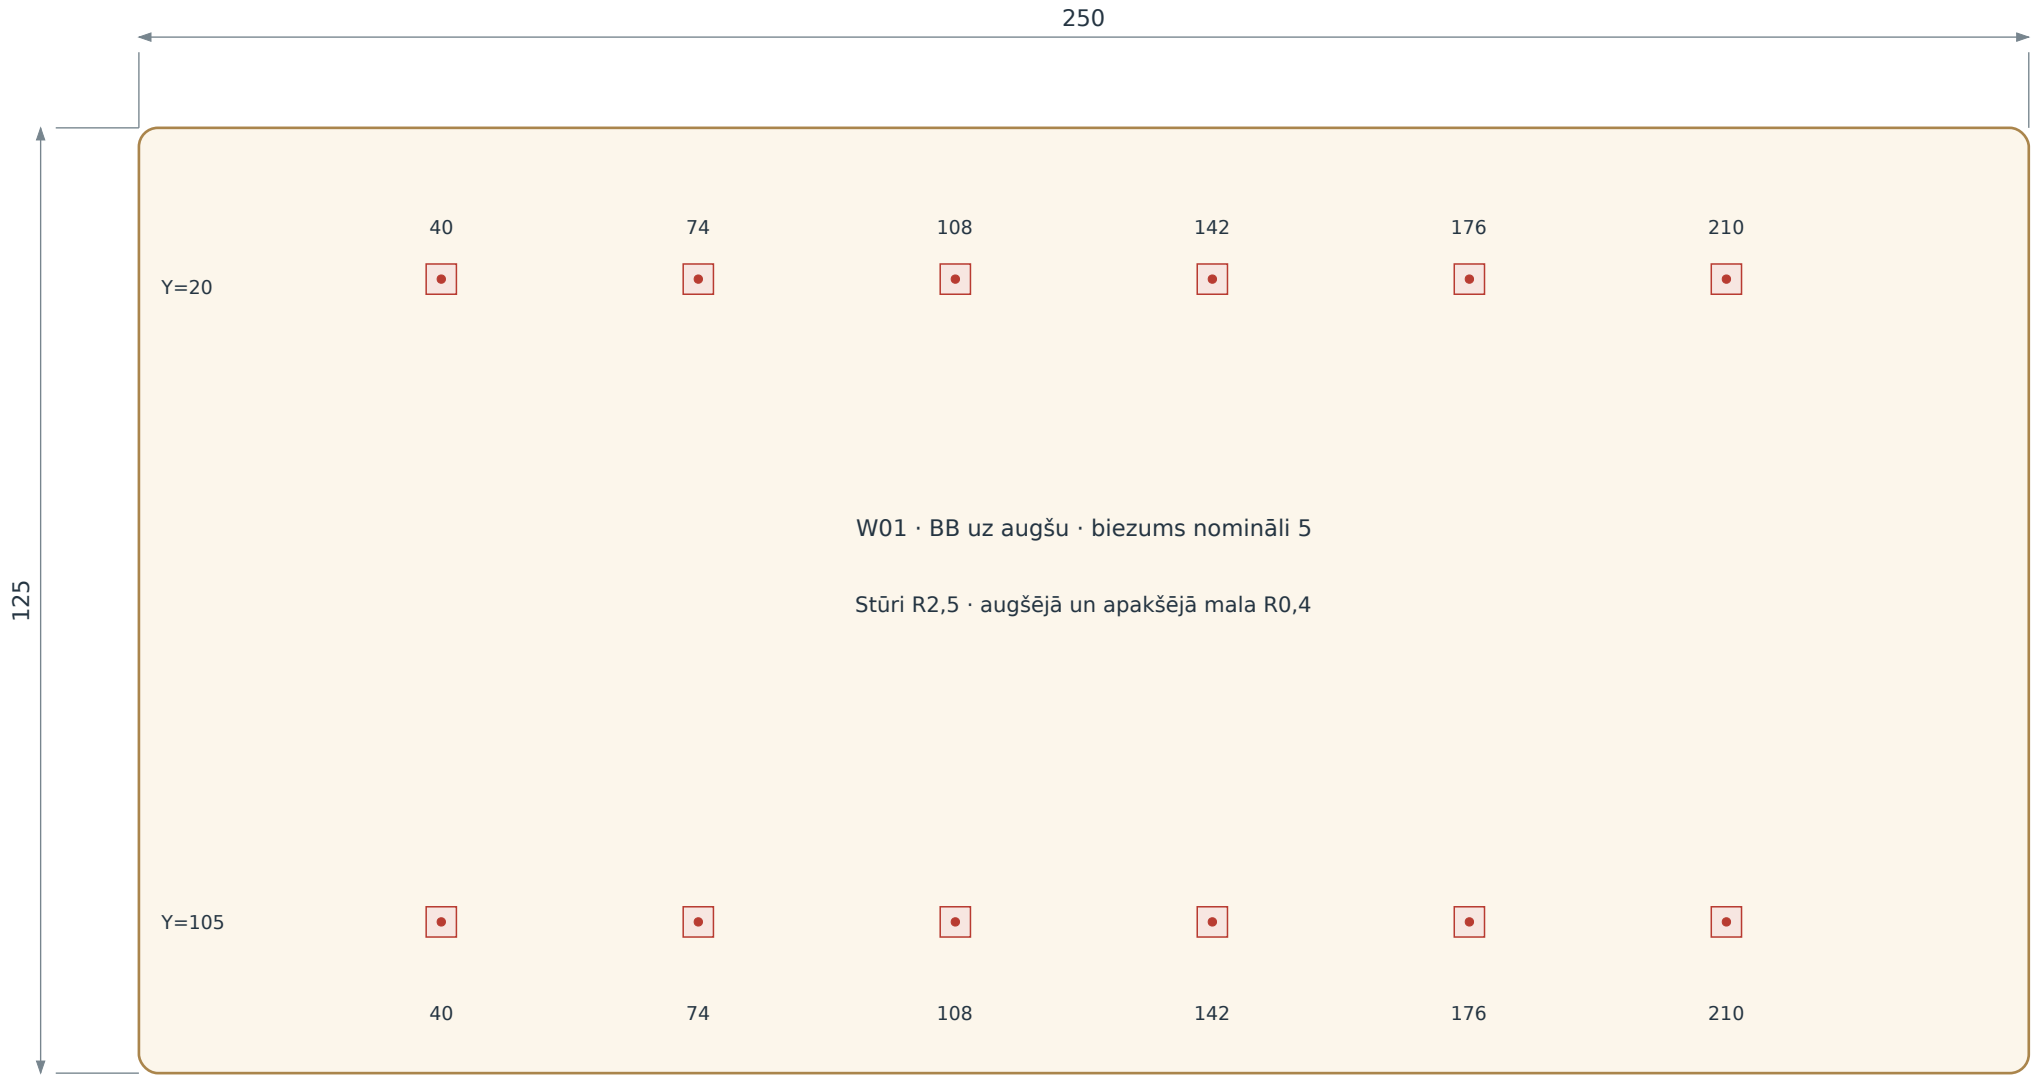

VIRSMA W01
12 M6 ieliktni, garums 1,8.
Urbuma dziļums līdz 2.
M6 skrūves garums 2.
Saķere nomināli 1,24.

PLAUKTA KLĀJS W05
150 × 35 × 1,8; stūri R1.
6 ieliktni, garums 1,2.
Urbuma dziļums līdz 1,3.
M6 skrūves garums 1,6.
Saķere nomināli 0,84.

Abiem: EPDM 0,2.
Urbuma Ø pēc ieliktna ražotāja.

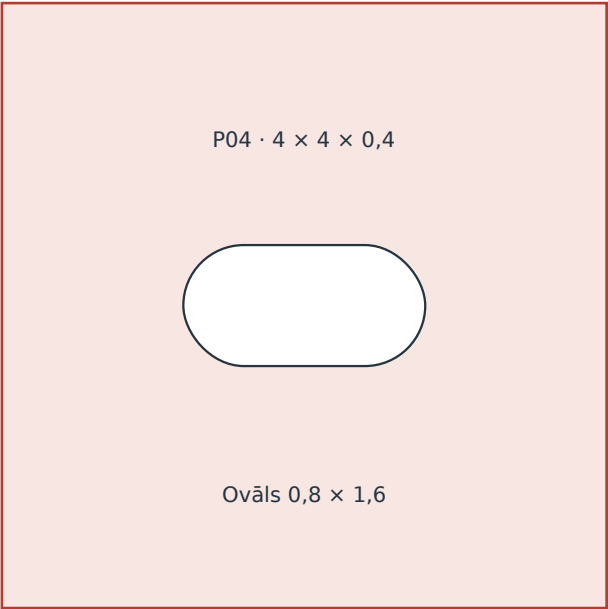


18 vienādas P04: 12 augšējā rāmī, 6 plaukta klājā.
Spraugas garenass X; centrs plāksnītes vidū.
P04 augša vienā plaknē ar attiecīgā rāmja augšu.

W05 urbumu centri: X=62; 116; 188 un Y=51; 74.
No W05 stūra (X=50; Y=45): x=12; 66; 138 un y=6; 29.
Koordinātas pārnēst pēc sausās montāžas; urbt no apakšas.
Plata paplāksne: Ø ap 1,8; biezums 0,16. Pārbaudīt saķeri.
Aizsargāt abas saplākšņa puses, malas un urbumus.

Plaukta savienojums ar kāju

P03 skats no plaukta puses, mērogs 1:1 · Četri mezgli; katrā divas skrūves M12

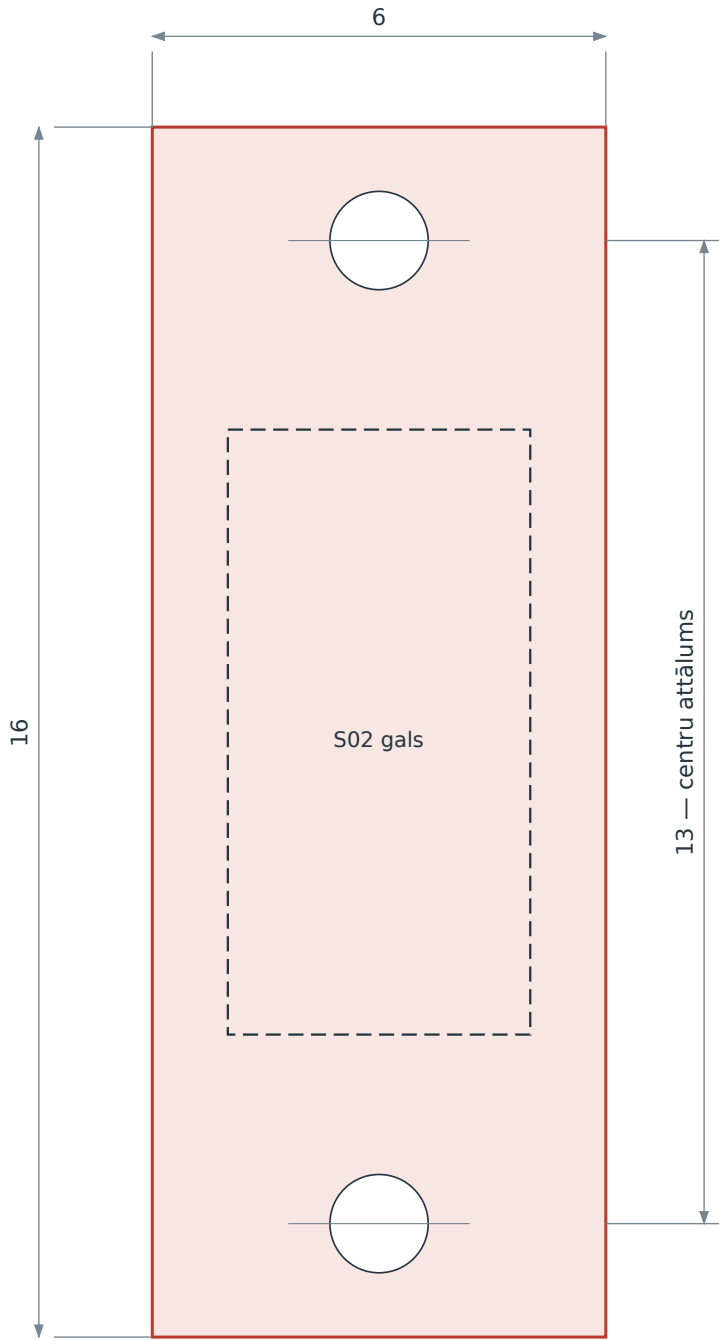

P03: 8 gab.; 16 × 6 × 0,8.
2 urbumi Ø1,3; X platuma centrā.
Centri 1,5 no augšas un apakšas.
P03 centrēta pret S02 galu.

IZVIETOJUMS UN MONTĀŽA

Fiksētā P03 piemetināta kājas iekšējai plaknei.
Noņemamā P03 piemetināta S02 galam.
Pa divām M12 skrūvēm, garums 3,5; paplāksne 0,25.
Uzgrieznis fiksētās P03 aizmugurē, kājas caurulē.
Pirms metināšanas kājas sienā izveidot divas Ø3 atveres.
Skrūves ievietot no plaukta puses; asis Y virzienā.

P03: Z=11–27; urbumu centri Z=12,5 un 25,5.
No kājas caurules apakšas: P03 apakša 7,2;
urbumu centri 8,7 un 21,7. Caurules apakša Z=3,8.

Kājām pie Y=20: fiksētā P03 Y=23–23,8;
noņemamā P03 Y=23,8–24,6.
Kājām pie Y=105: fiksētā P03 Y=101,2–102;
noņemamā P03 Y=100,4–101,2.

Kāju iekšējo plakņu attālums: 79.
 $0,8 + 0,8 + 75,8 + 0,8 + 0,8 = 79$.
M12 saķerei aiz fiksētās plāksnes paliek 1,65.
Uzgriežņa un šuves apvalku pārbaudīt pirms urbšanas.

P03 sānu šuves nepārtrauktas pa visu pieejamo garumu.
S02 gala šuve pie noņemamās P03 pa visu caurules perimetru.
Montēt šablonā; plāksnēm cieši jāsaskaras bez siju piespiedu liekšanas.
Galīgo metinājumu un savienojumu pārbauda kompetents izgatavotājs.